Demo Project

mid_ex882

April 11, 2026

UniFi Devices	Quantity
E7	1
U6 Pro	3

Floor Plan

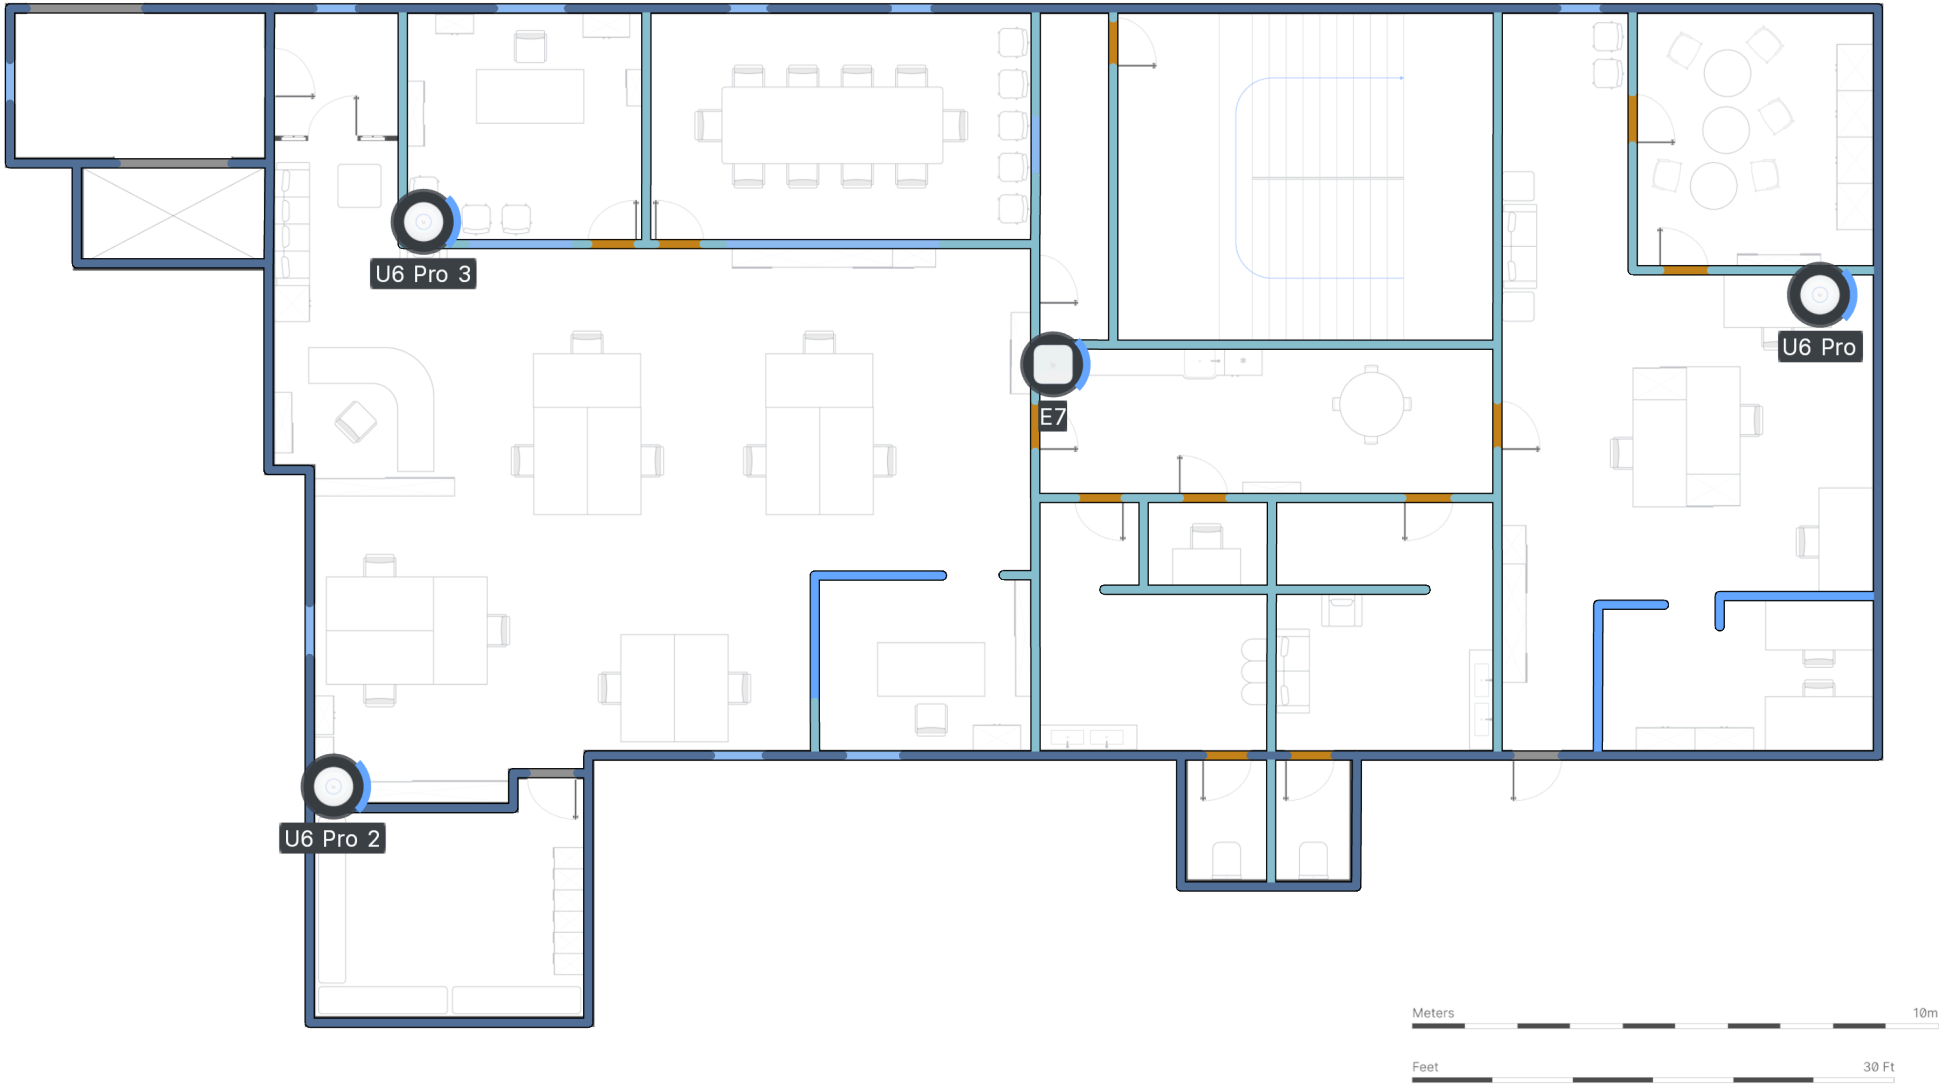

Estimated 2.4GHz WiFi Coverage

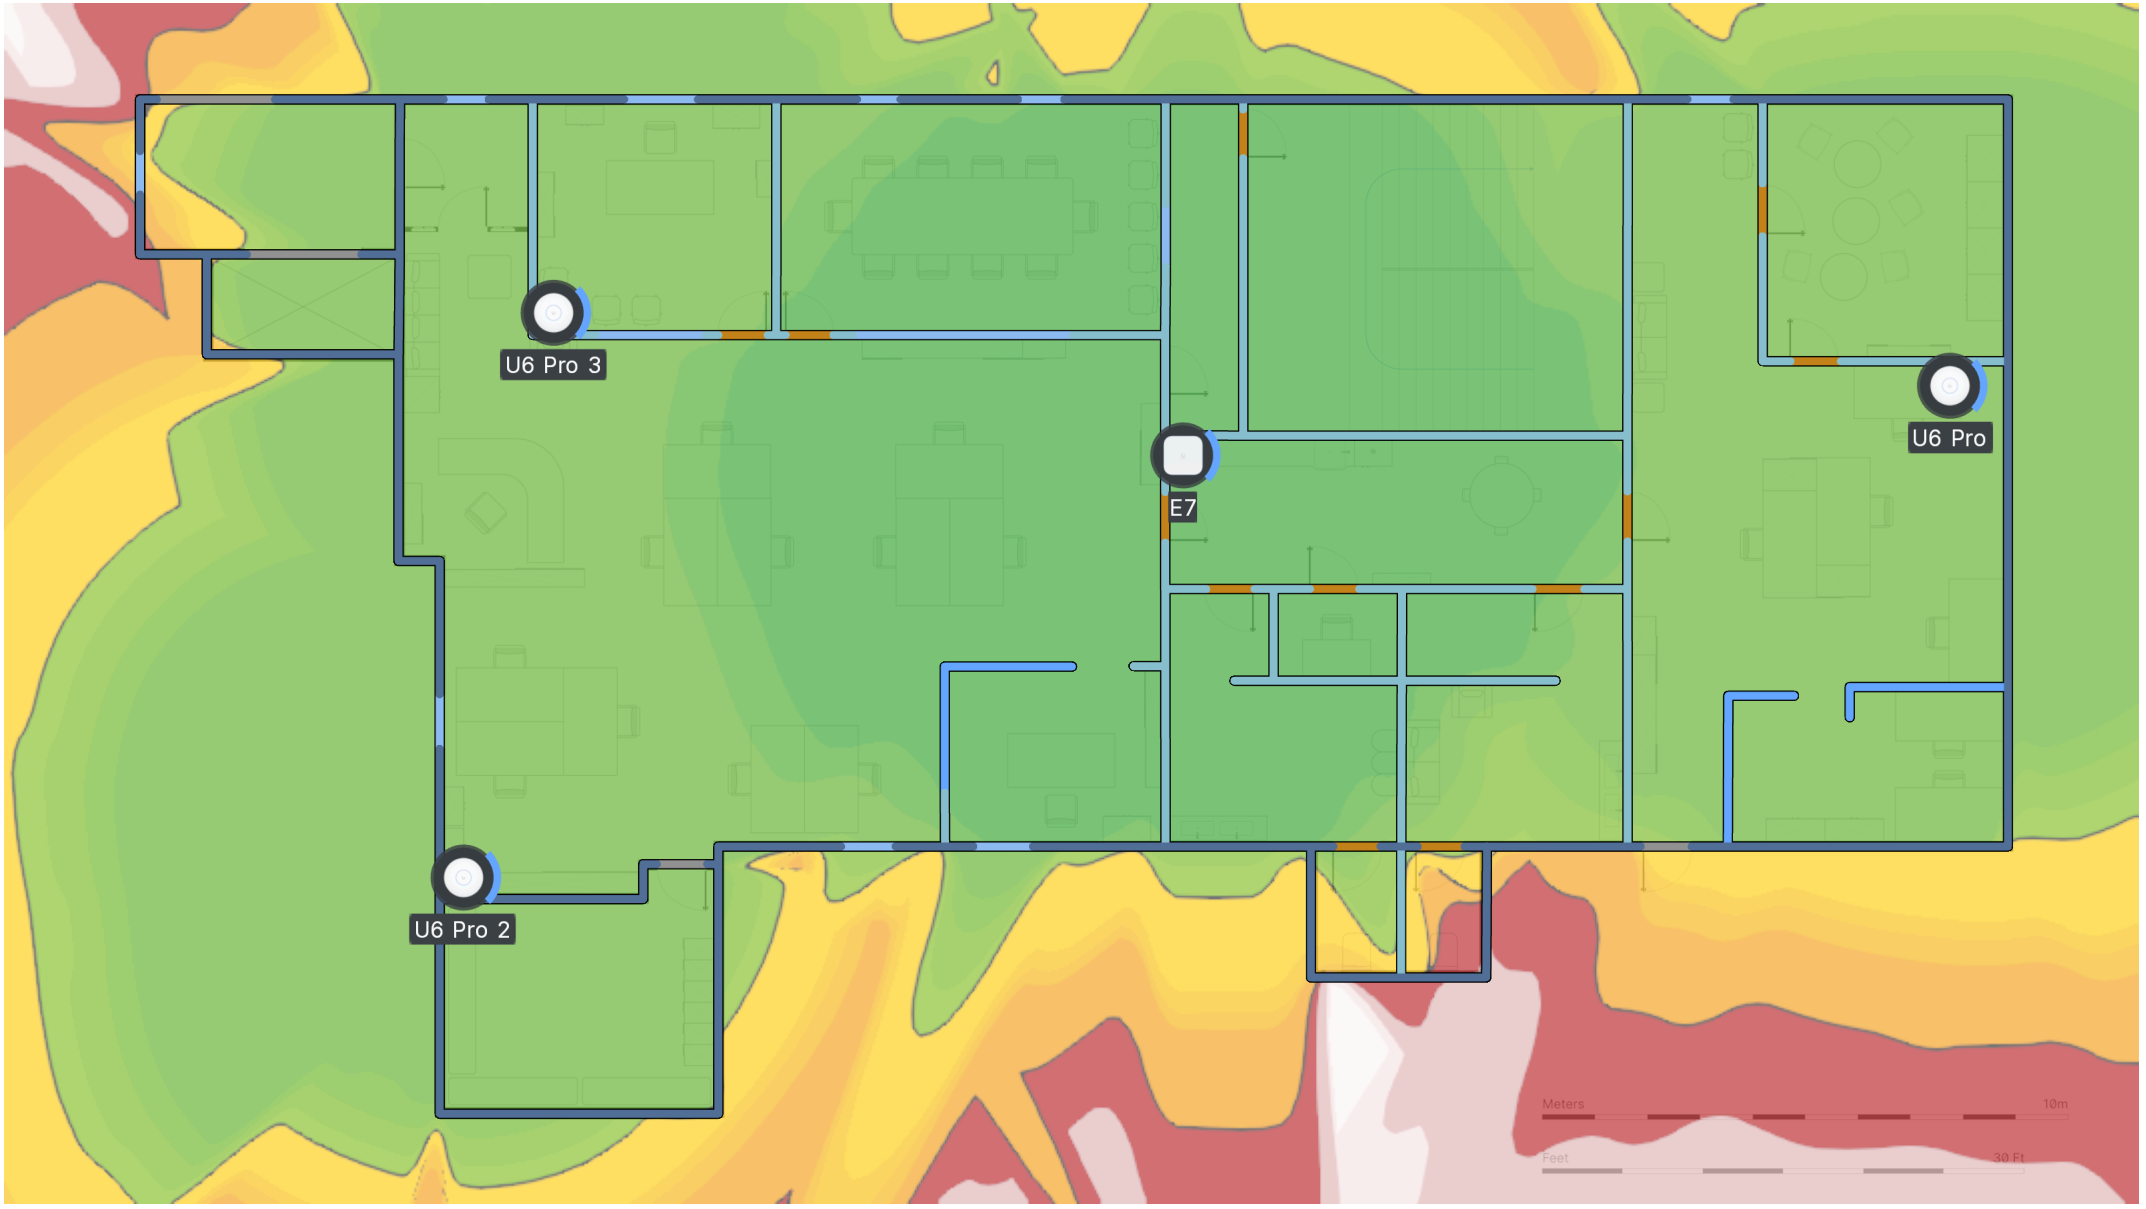

Estimated 5GHz WiFi Coverage

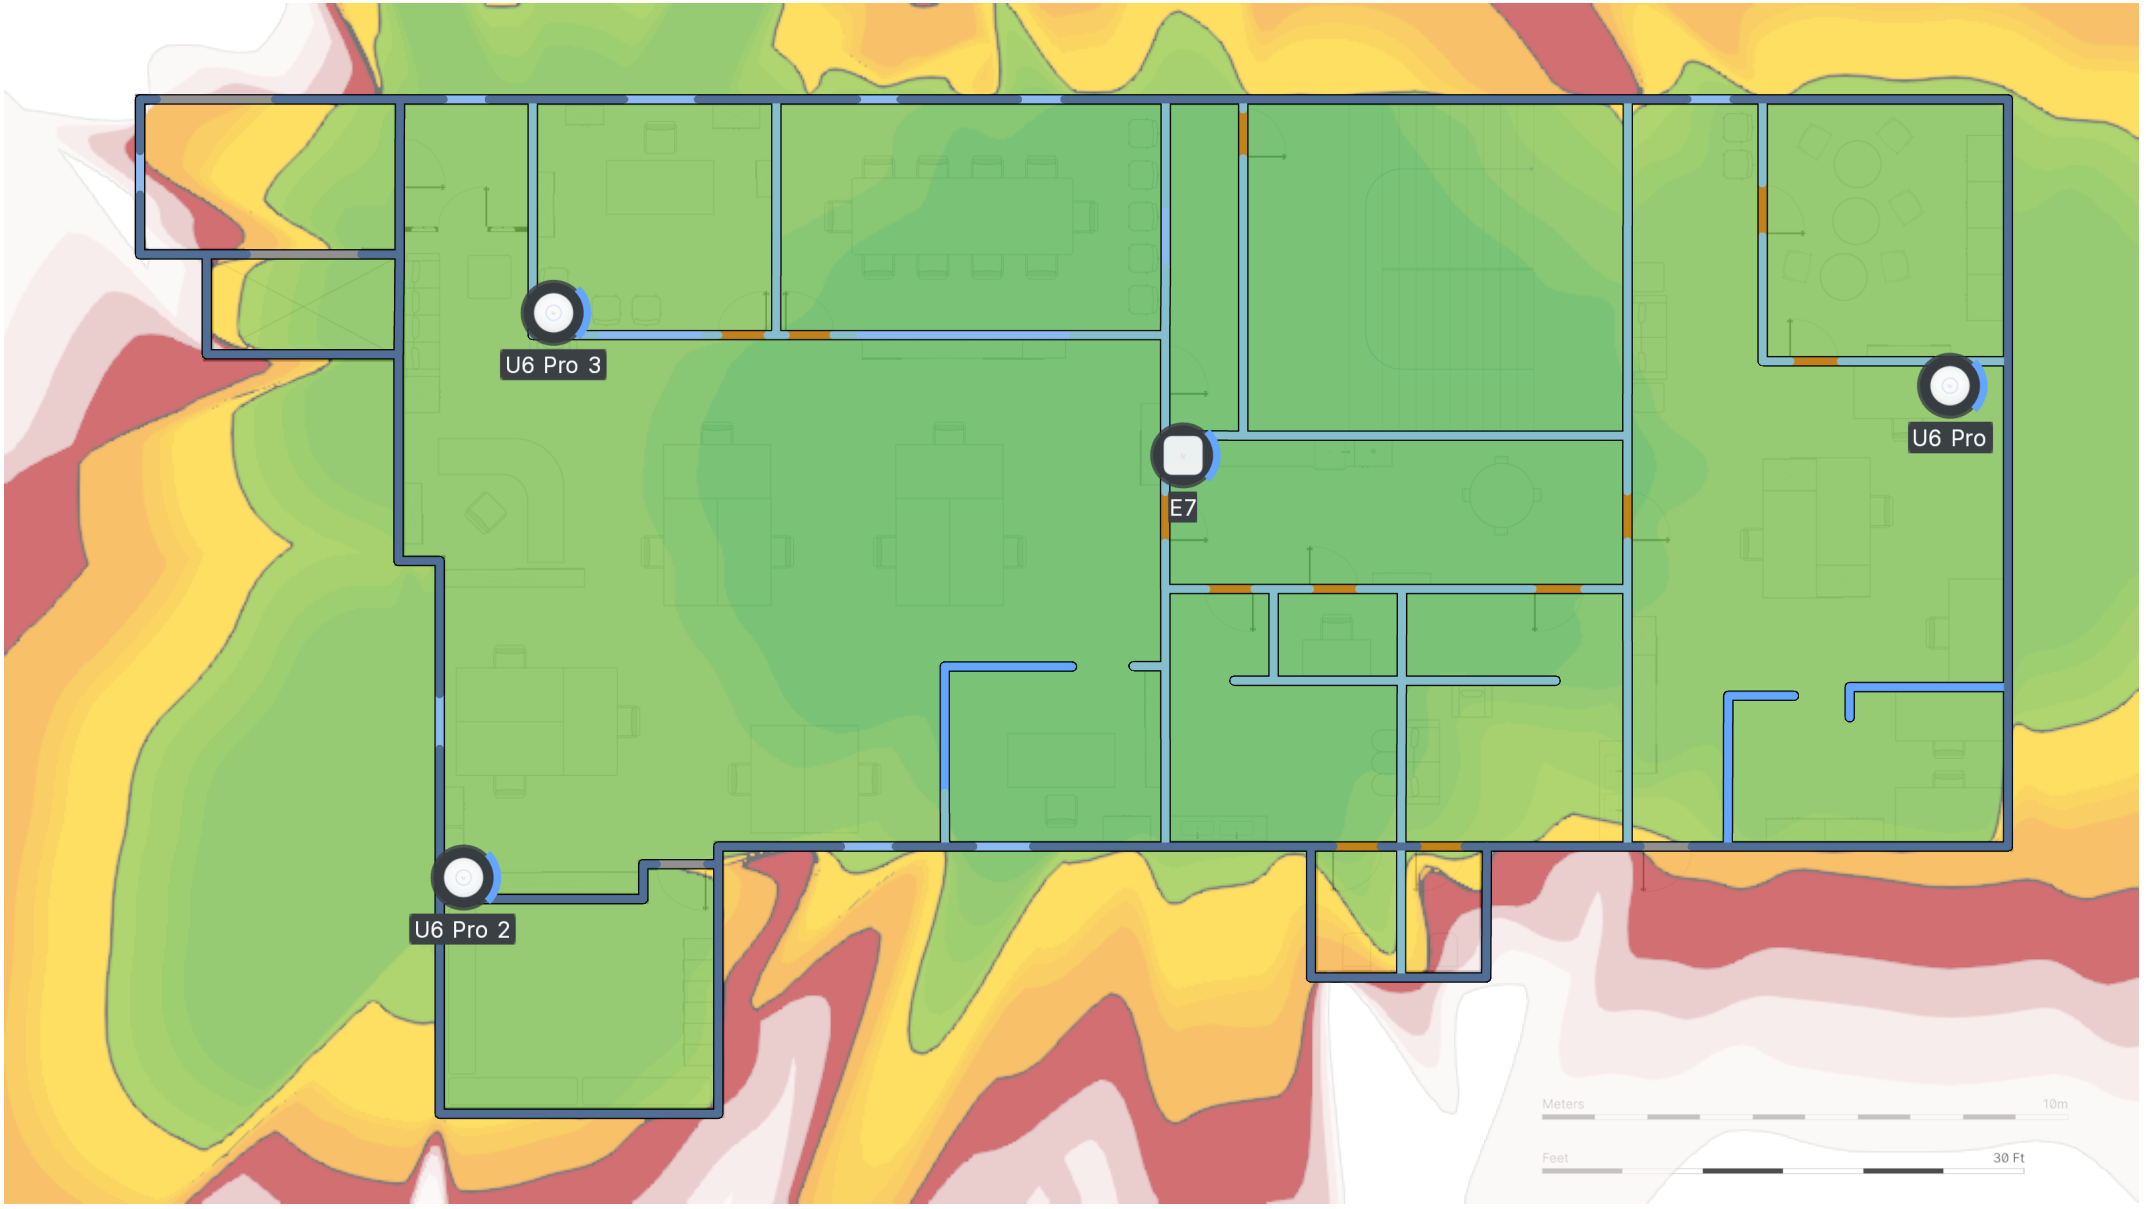
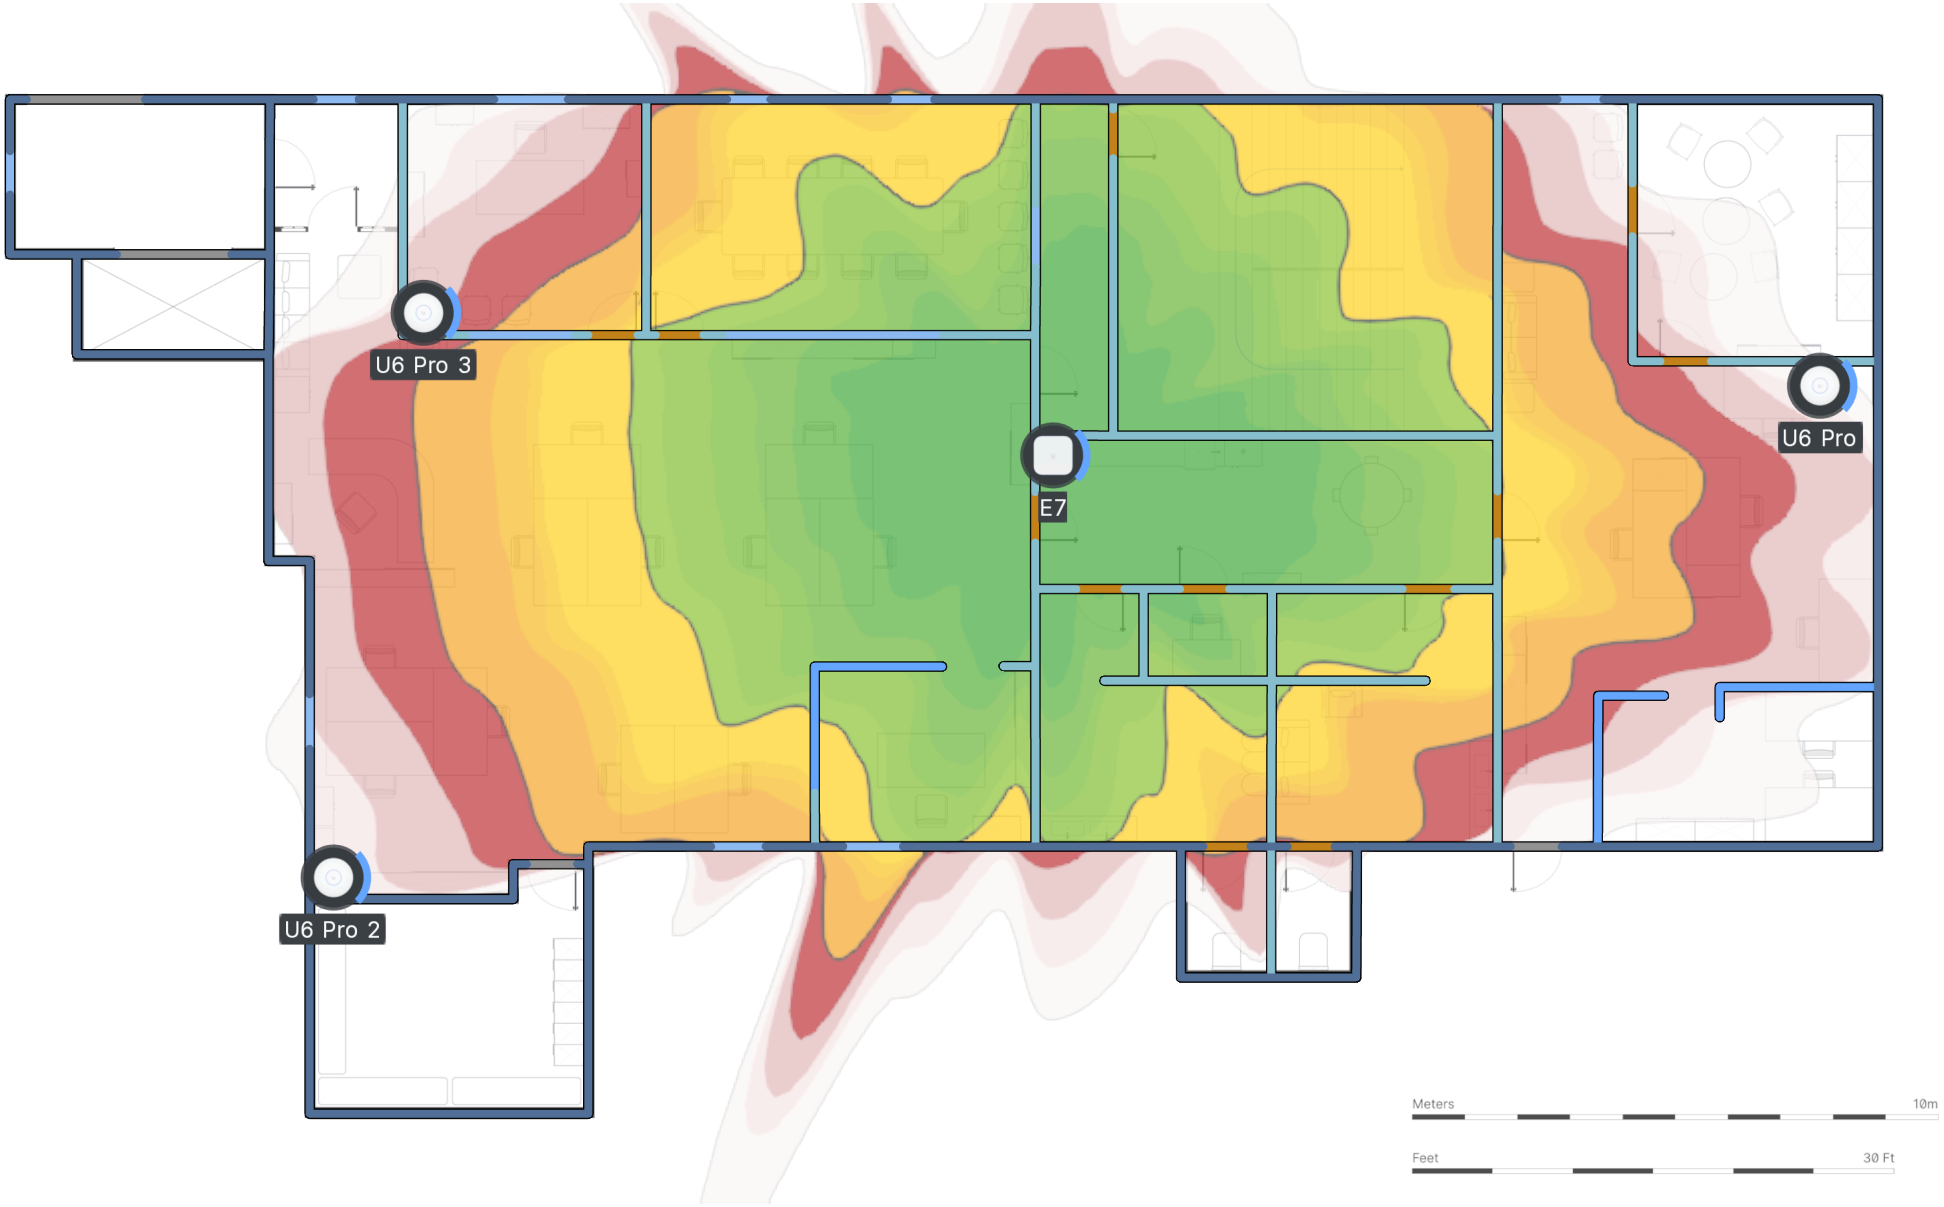
Estimated 6GHz WiFi Coverage