Demo Project

mid_ex882

April 11, 2026

UniFi Devices	Quantity
Enterprise Fortress Gateway	2
Enterprise NVR	1
Enterprise Campus Aggregation	2
24-Port Blank Keystone Patch Panel	12
Enterprise Campus 48 PoE	6
G6 Pro Dome	15
G6 Pro 360	4
AI LPR	3
Power Distribution Pro	2
E7	50
E7 Campus	15
E7 Audience	10
G3 Reader Pro	10
G3 Intercom	3
Intercom Viewer	5
Door Hub	3
Enterprise Access Hub	1
Gate Hub	3
G6 Pro Bullet	30

Communications Rack	Quantity
42U Rack Cabinet	1

UniFi Devices	Quantity
U6 Pro	3

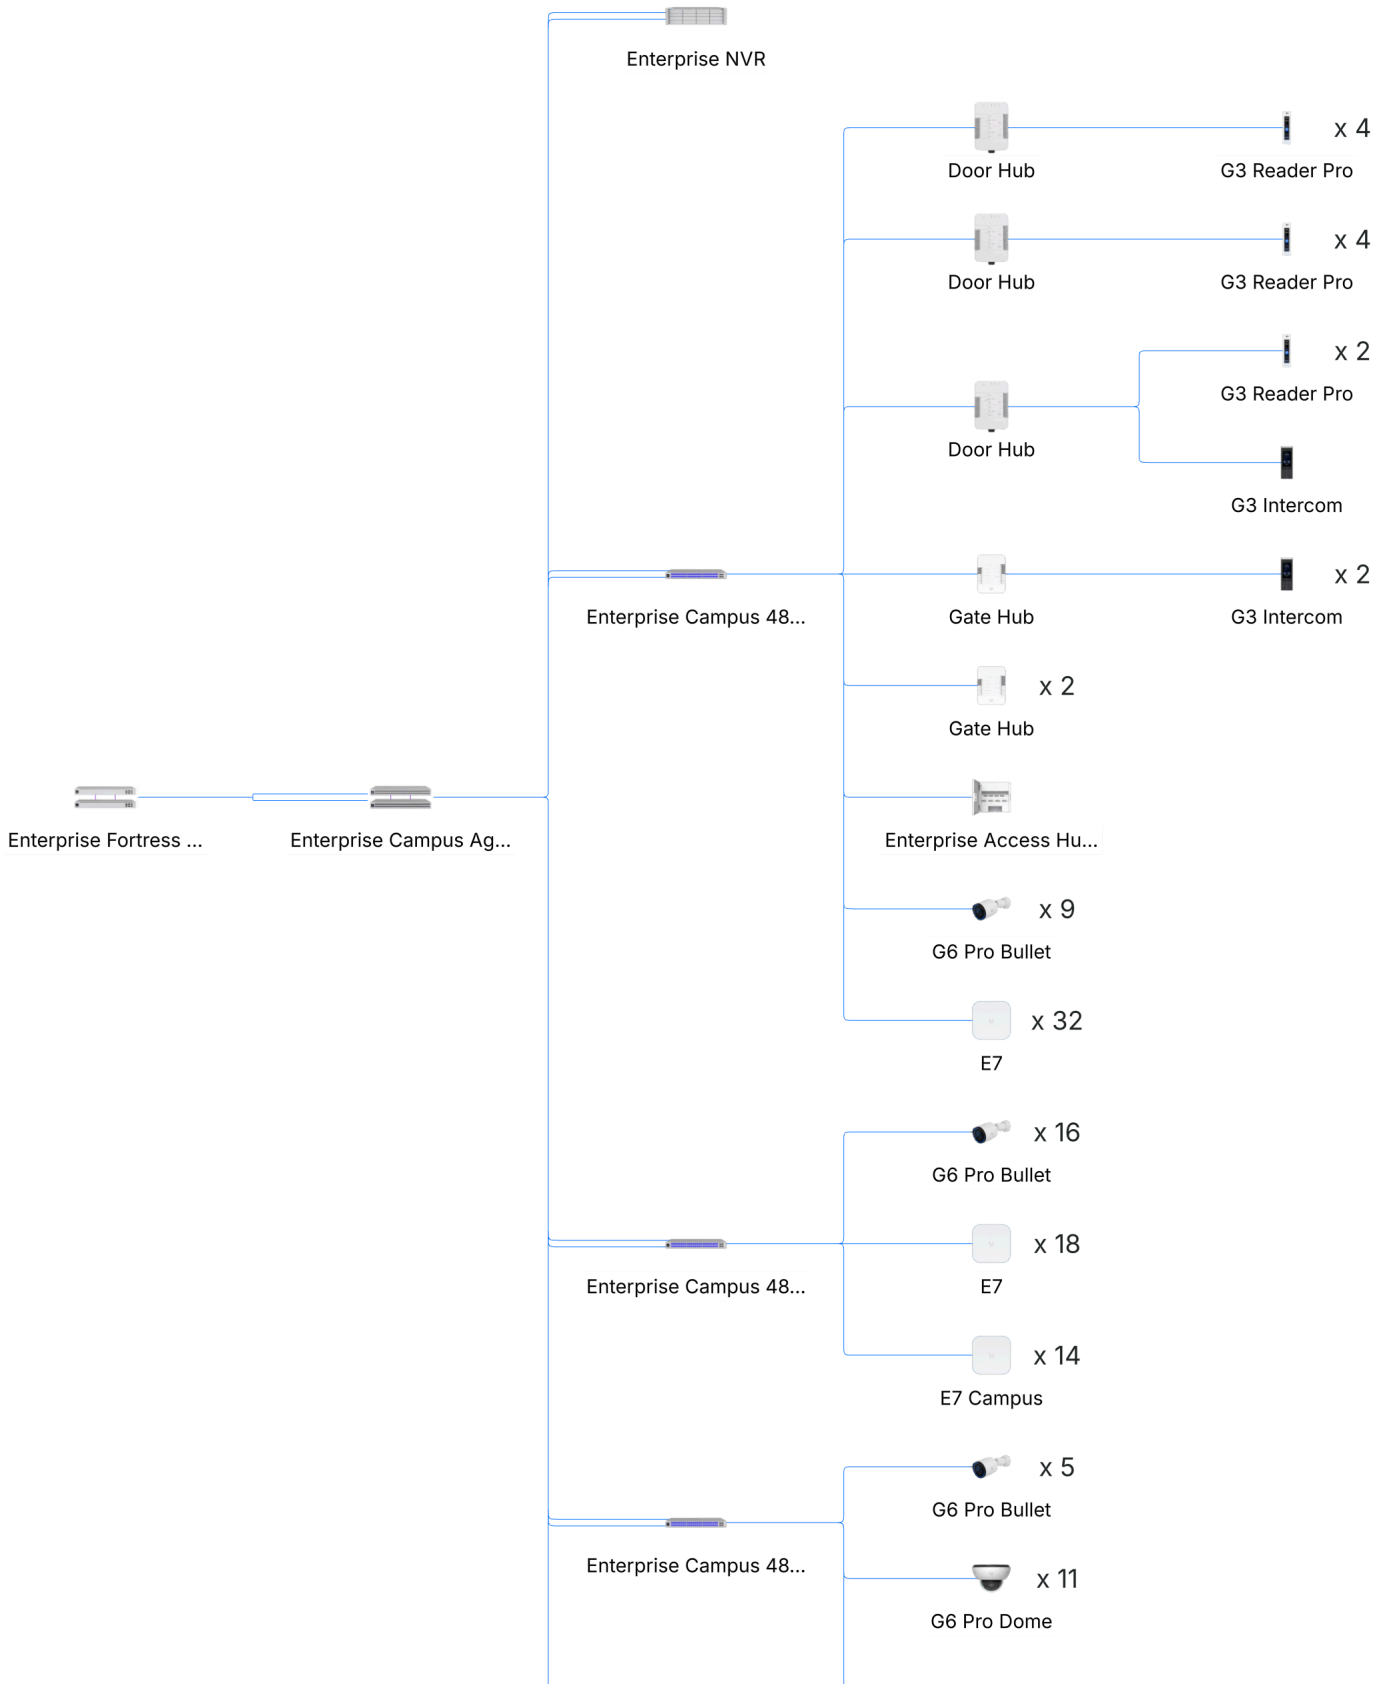
Enterprise NVR
Door Hub
x 4
G3 Reader Pro
Door Hub
x 4
G3 Reader Pro
x 2
G3 Reader Pro
Door Hub
G3 Intercom
Enterprise Campus 48...
Gate Hub
x 2
G3 Intercom
x 2
Gate Hub
Enterprise Fortress ...
Enterprise Campus Ag...
Enterprise Access Hu...
x 9
G6 Pro Bullet
x 32
E7
x 16
G6 Pro Bullet
Enterprise Campus 48...
x 18
E7
x 14
E7 Campus
x 5
G6 Pro Bullet
Enterprise Campus 48...
x 11
G6 Pro Dome

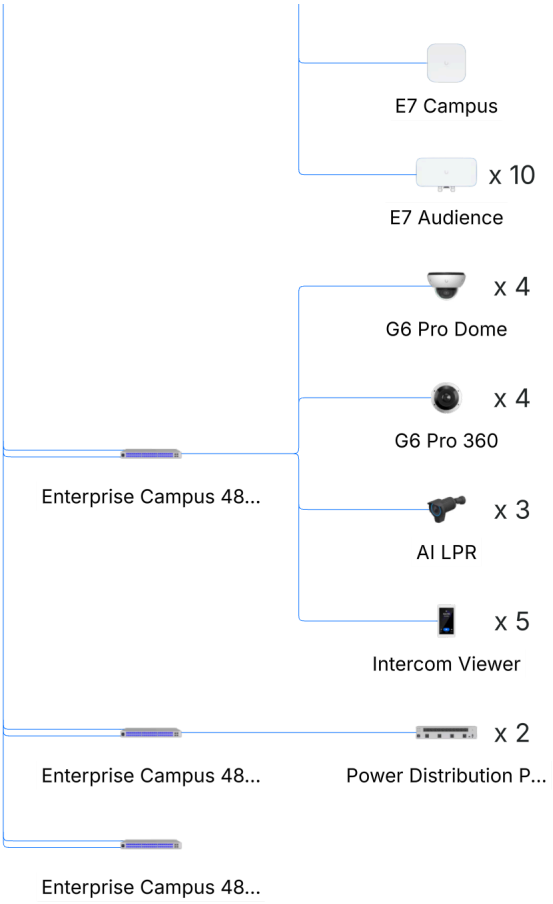
E7 Campus
x 10
E7 Audience
x 4
G6 Pro Dome
x 4
G6 Pro 360
Enterprise Campus 48...
x 3
AI LPR
x 5
Intercom Viewer
x 2
Enterprise Campus 48...
Power Distribution P...
Enterprise Campus 48...

Floor Plan

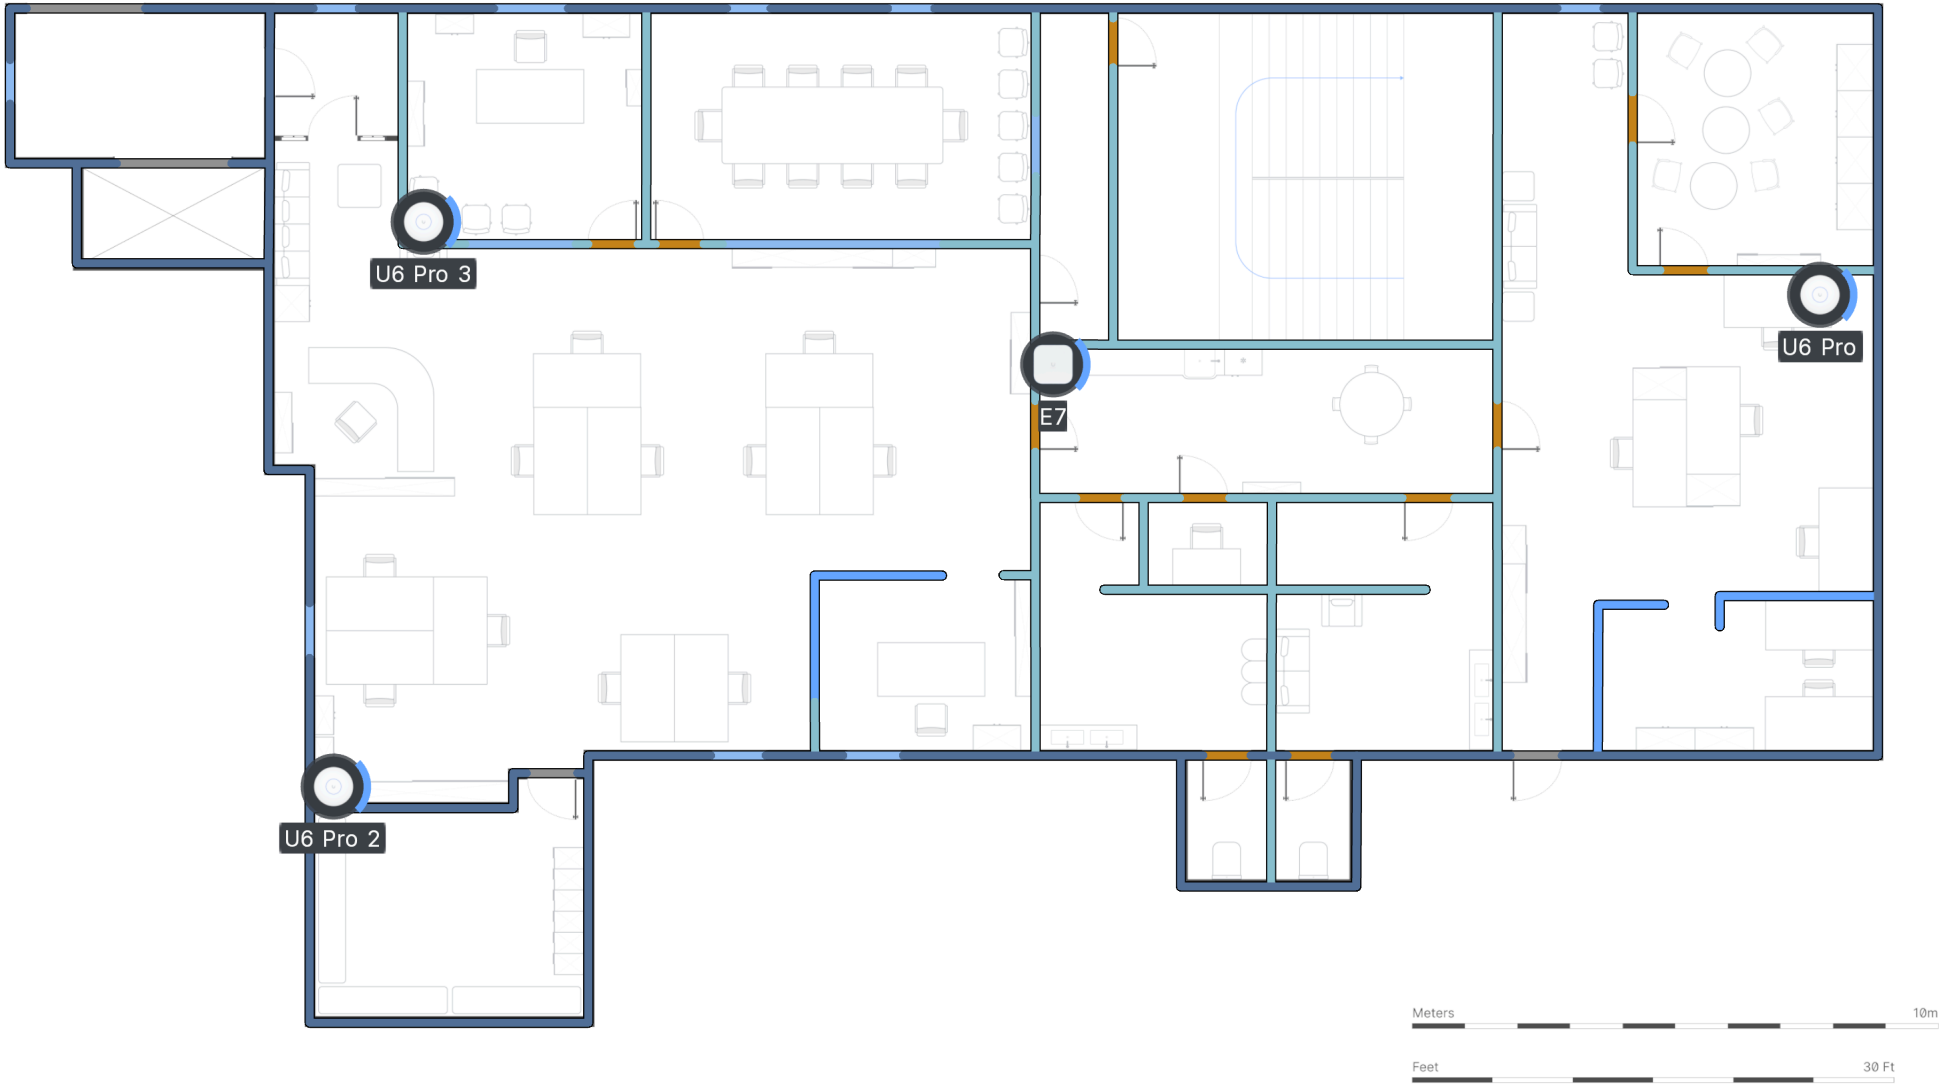

Estimated 2.4GHz WiFi Coverage

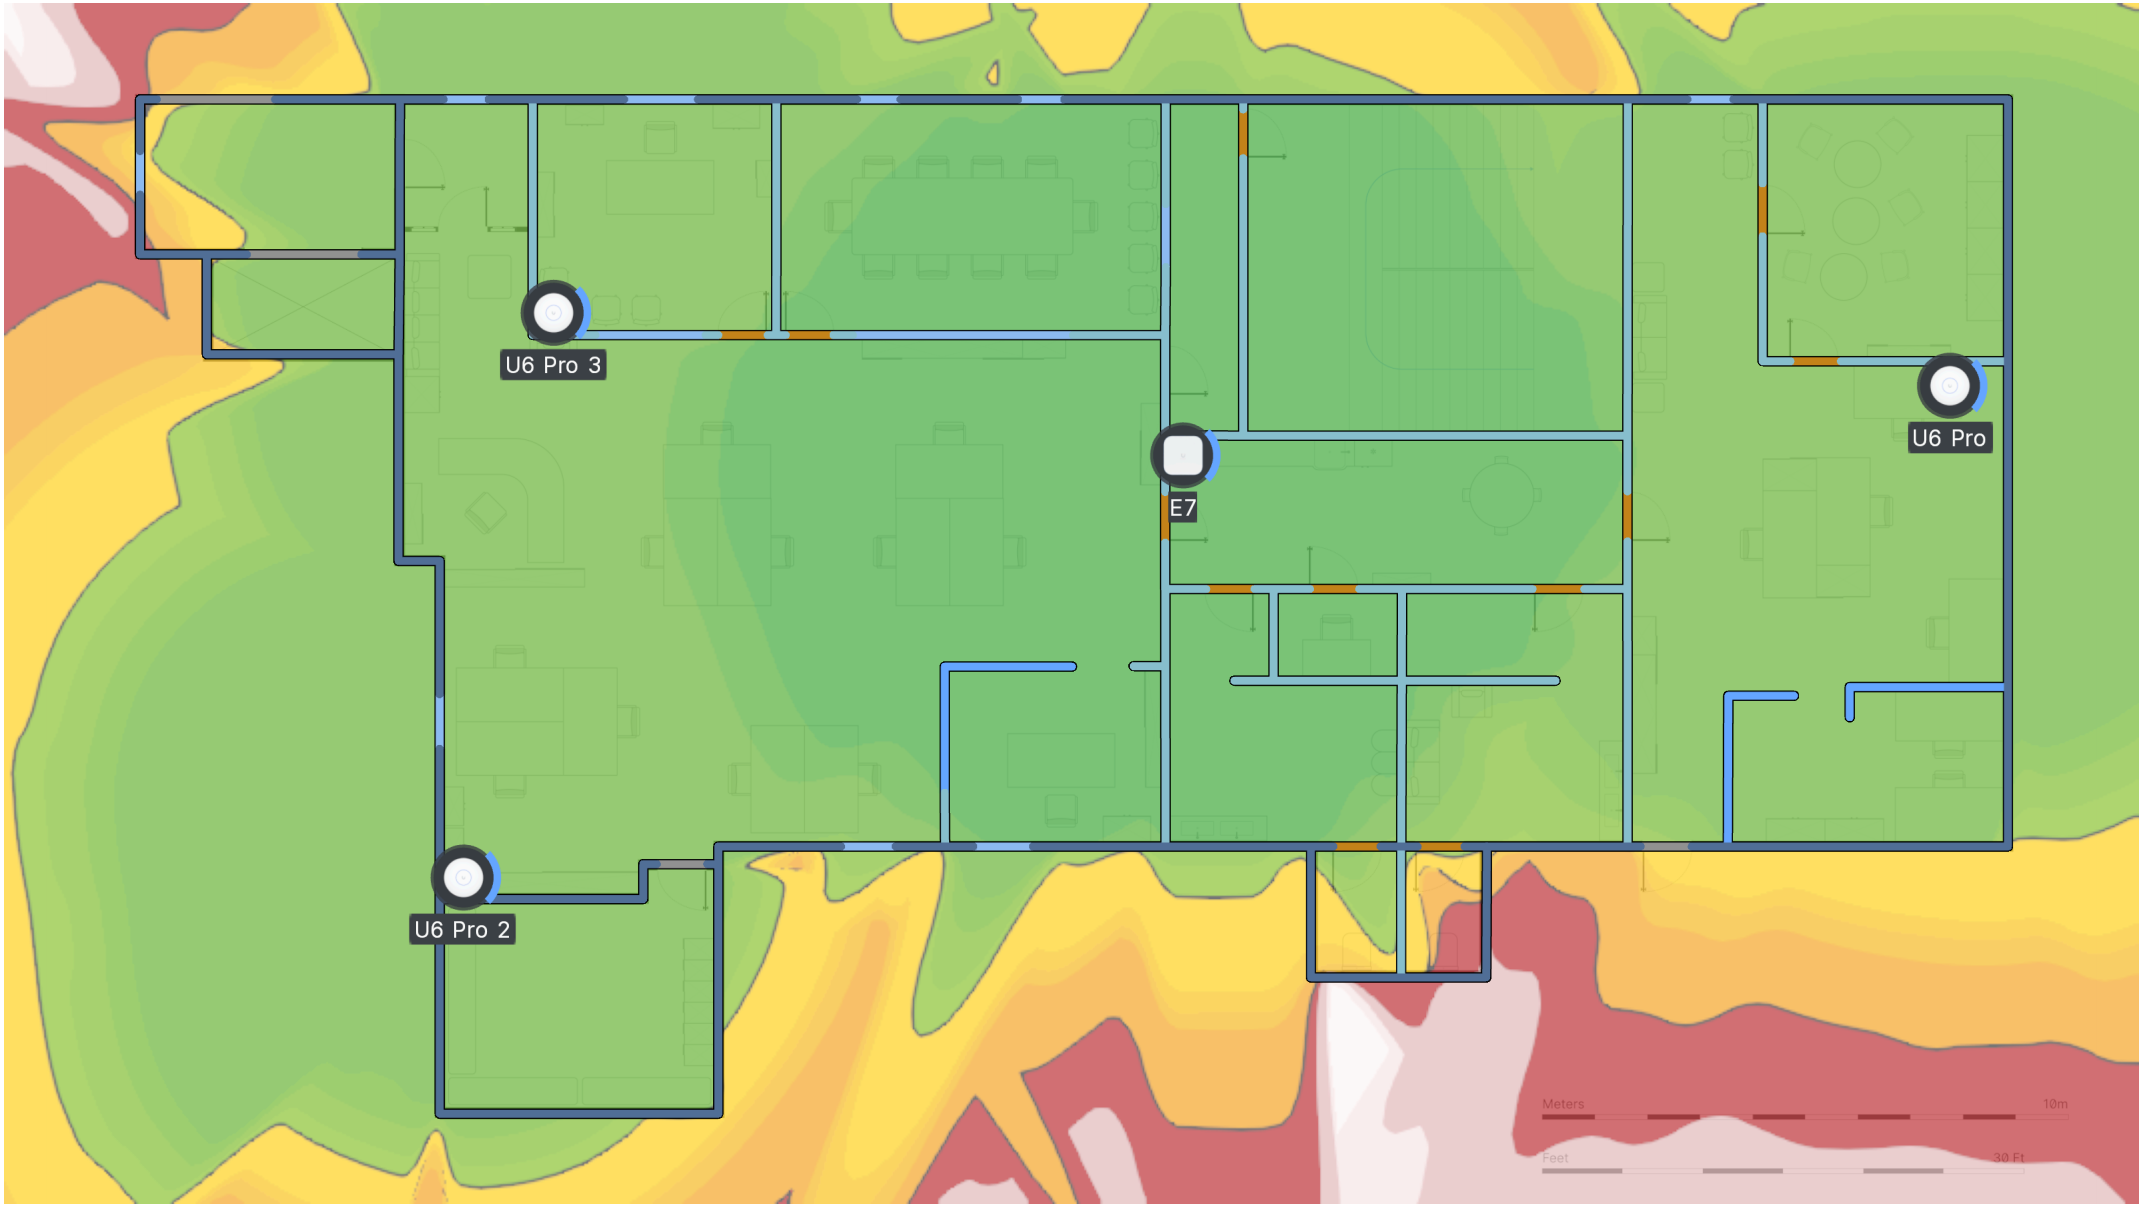

Estimated 5GHz WiFi Coverage

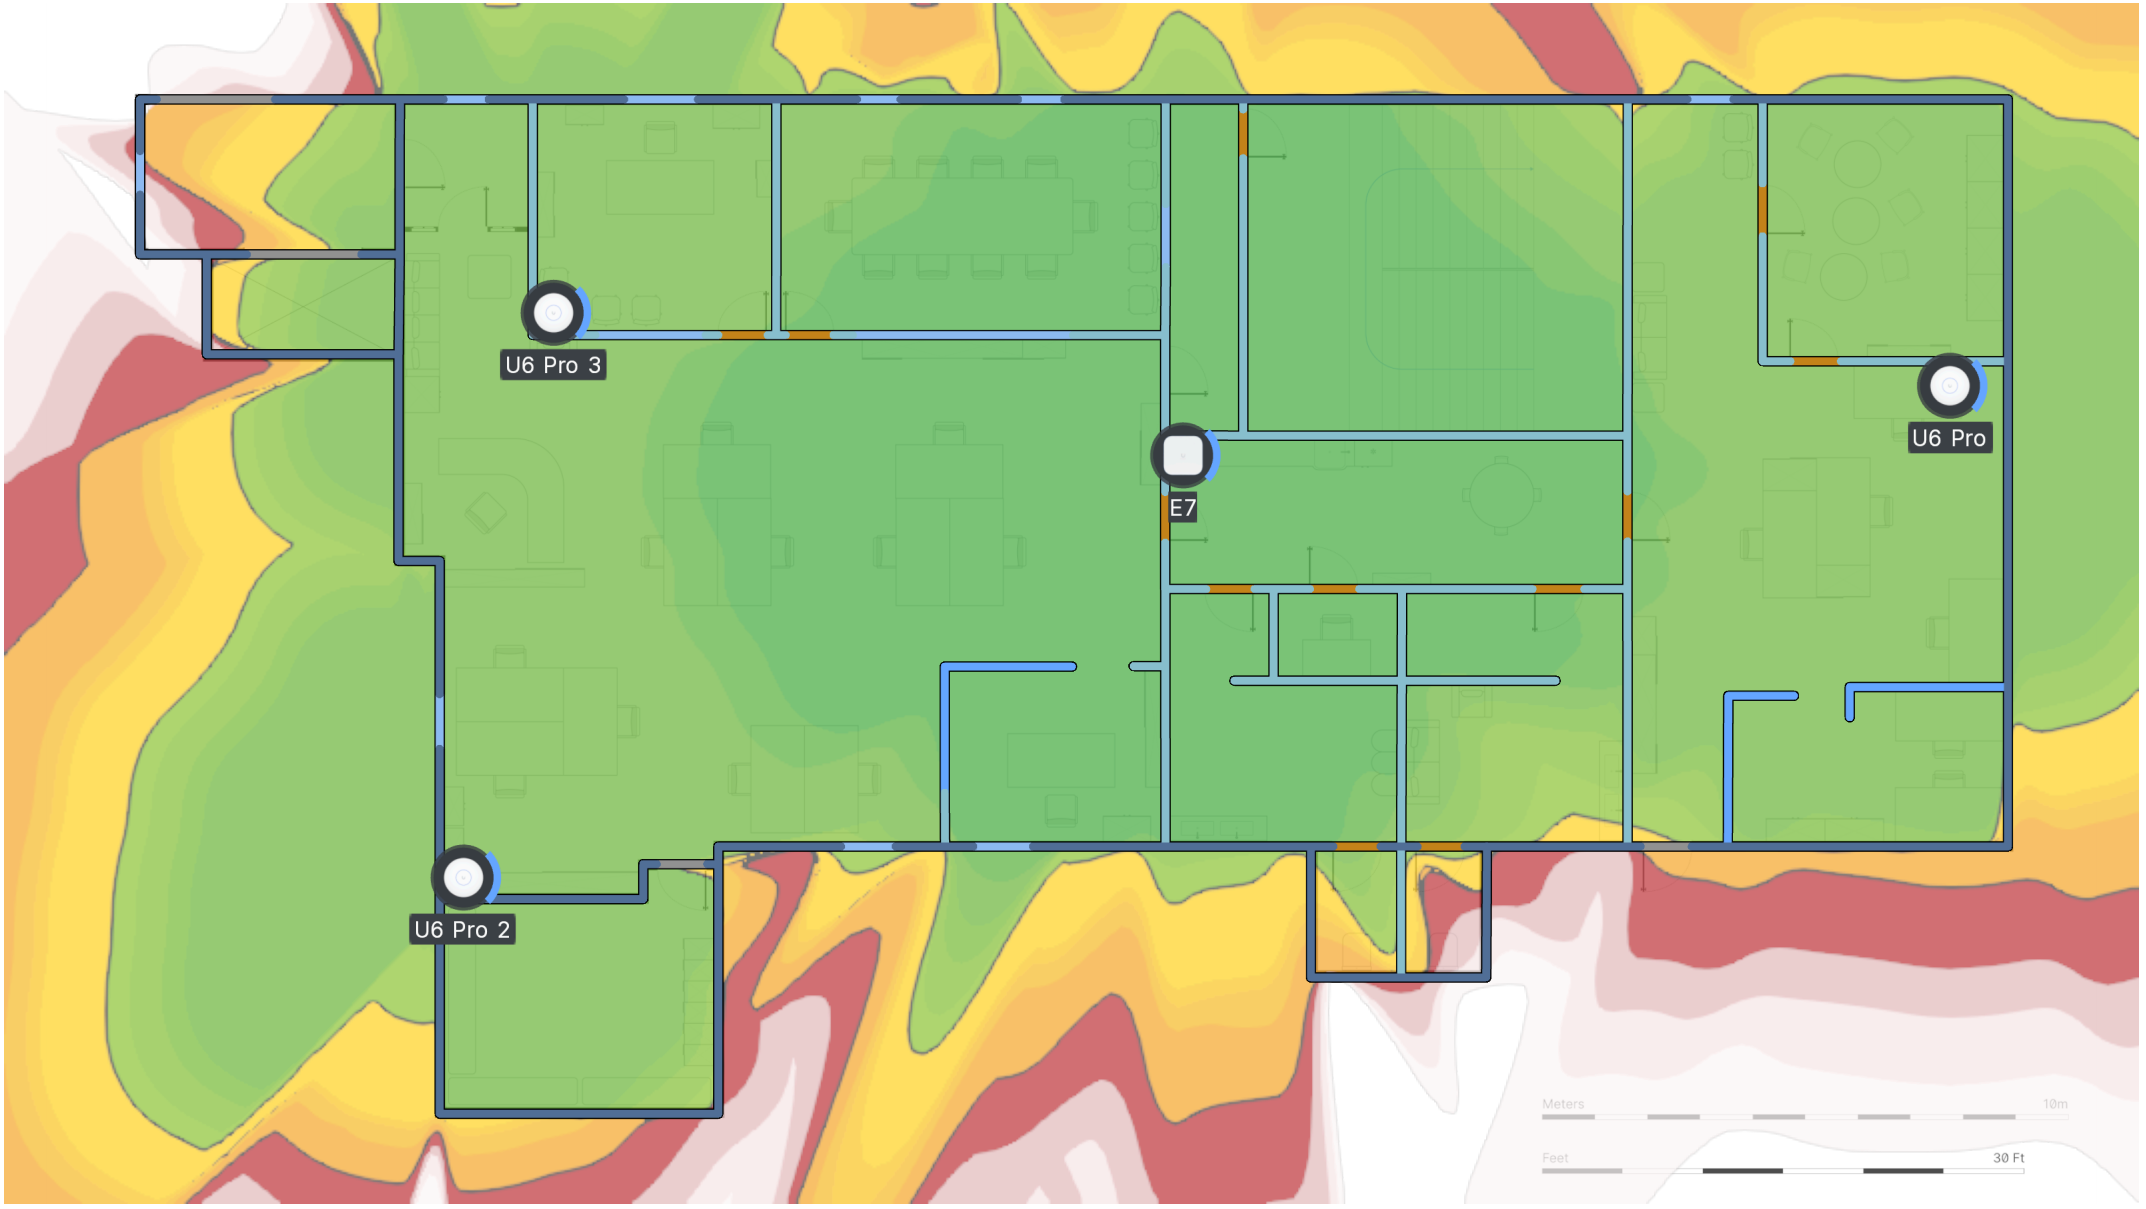

Estimated 6GHz WiFi Coverage

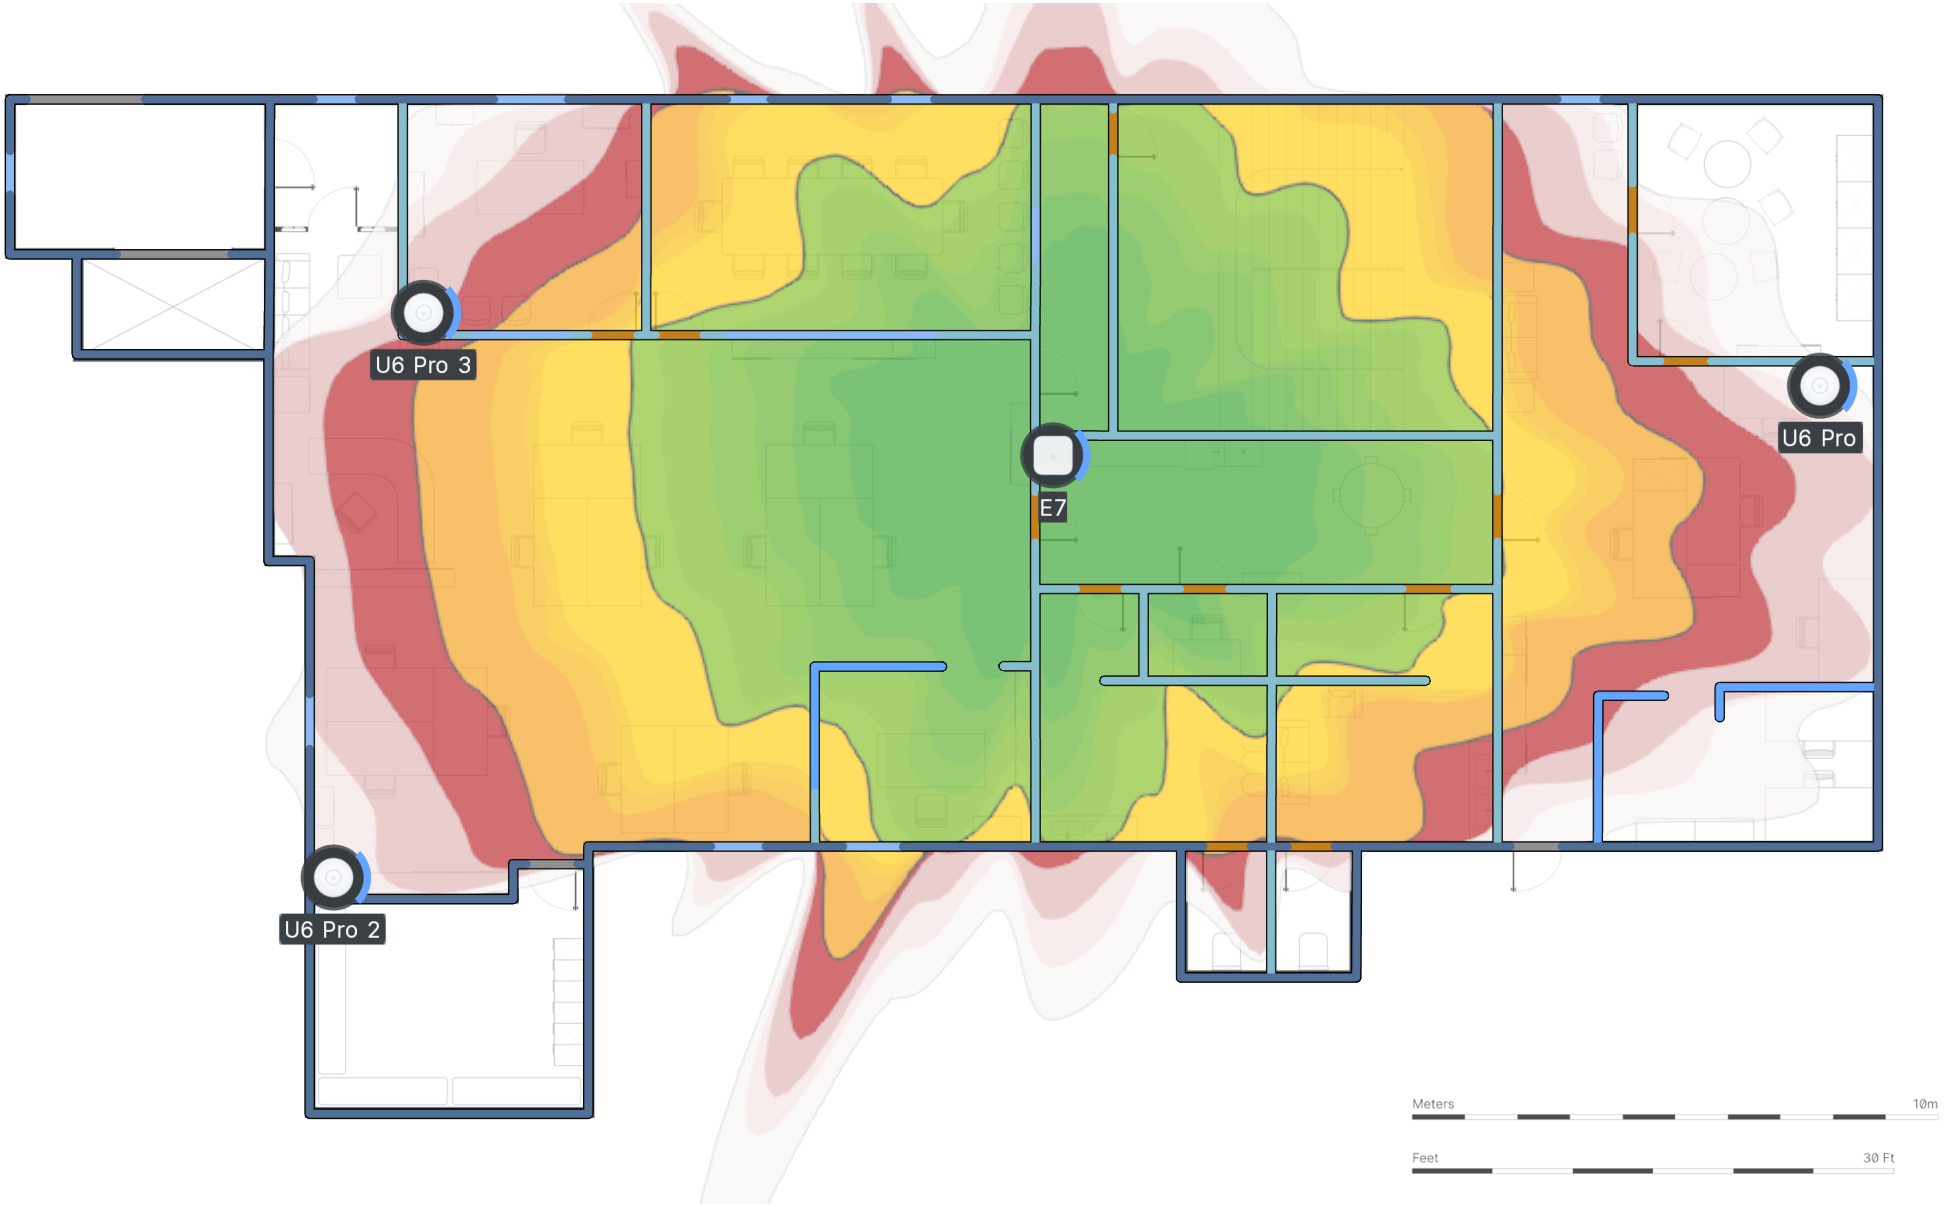

Ports 183/437

Power 4399.56/12900W

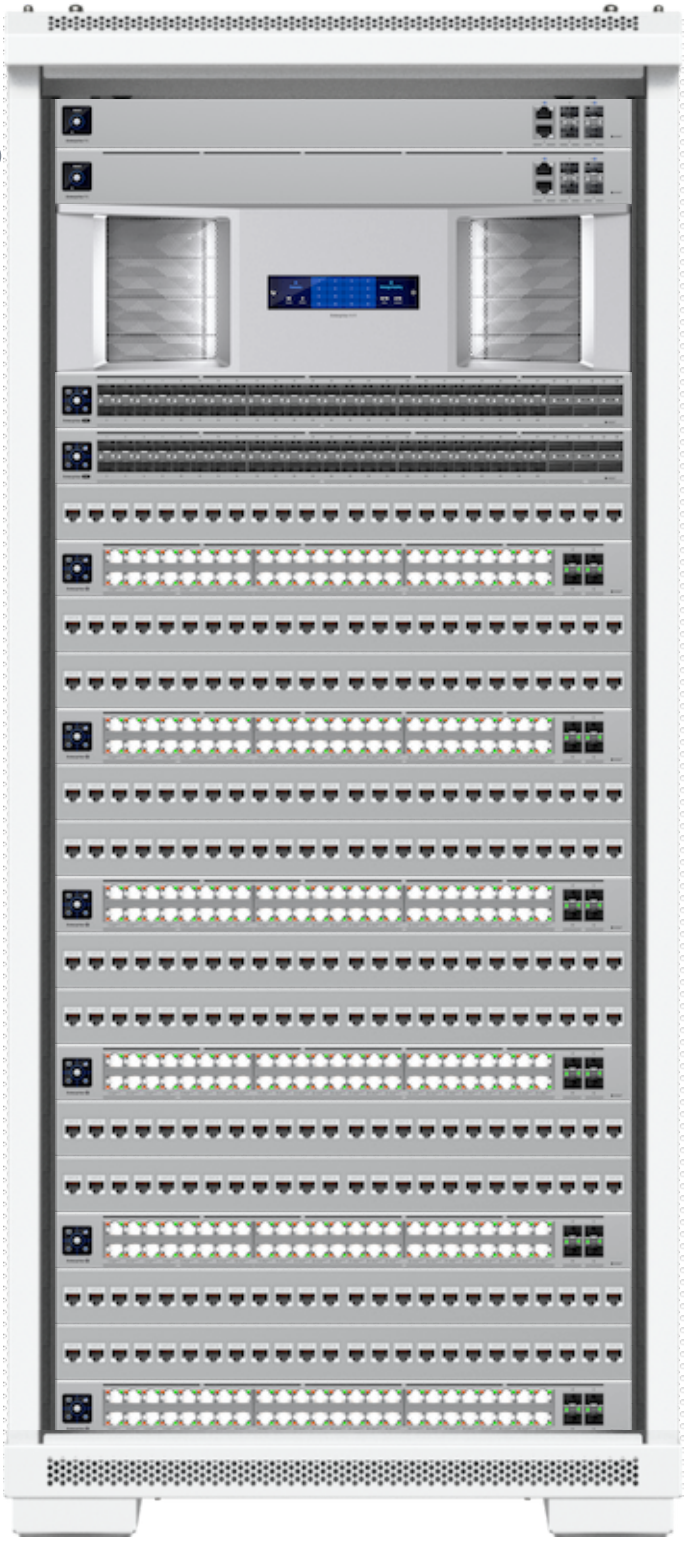

- A Enterprise Fort...
- B Enterprise Fort...
- C Enterprise NVR
- D Enterprise Ca...
- E Enterprise Ca...
- 24-Port Blank Keys...
- F Enterprise Ca...
- 24-Port Blank Keys...
- 24-Port Blank Keys...
- G Enterprise Ca...
- 24-Port Blank Keys...
- 24-Port Blank Keys...
- H Enterprise Ca...
- 24-Port Blank Keys...
- 24-Port Blank Keys...
- I Enterprise Ca...
- 24-Port Blank Keys...
- 24-Port Blank Keys...
- J Enterprise Ca...
- 24-Port Blank Keys...
- 24-Port Blank Keys...
- K Enterprise Ca...

Ports 183/437

Power 4399.56/12900W

24-Port Blank Keys...

Power Distribution ...

Power Distribution ...

A Enterprise Fortress Gateway

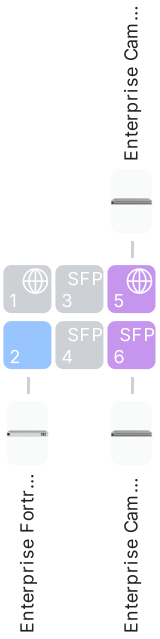

B Enterprise Fortress Gateway

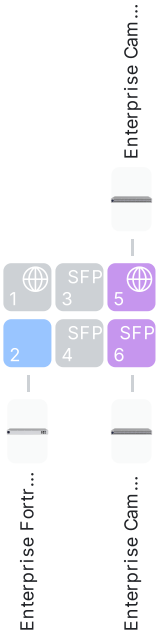

GbE 2.5 GbE 10 GbE 25 GbE 100 GbE PoE PoE+ PoE++ PoE+++ WAN

C Enterprise NVR

D Enterprise Campus Aggregation

GbE 2.5 GbE 10 GbE 25 GbE 100 GbE PoE PoE+ PoE++ PoE+++
WAN

E Enterprise Campus Aggregation

F Enterprise Campus 48 PoE

PoE Power Used 1722/2150W

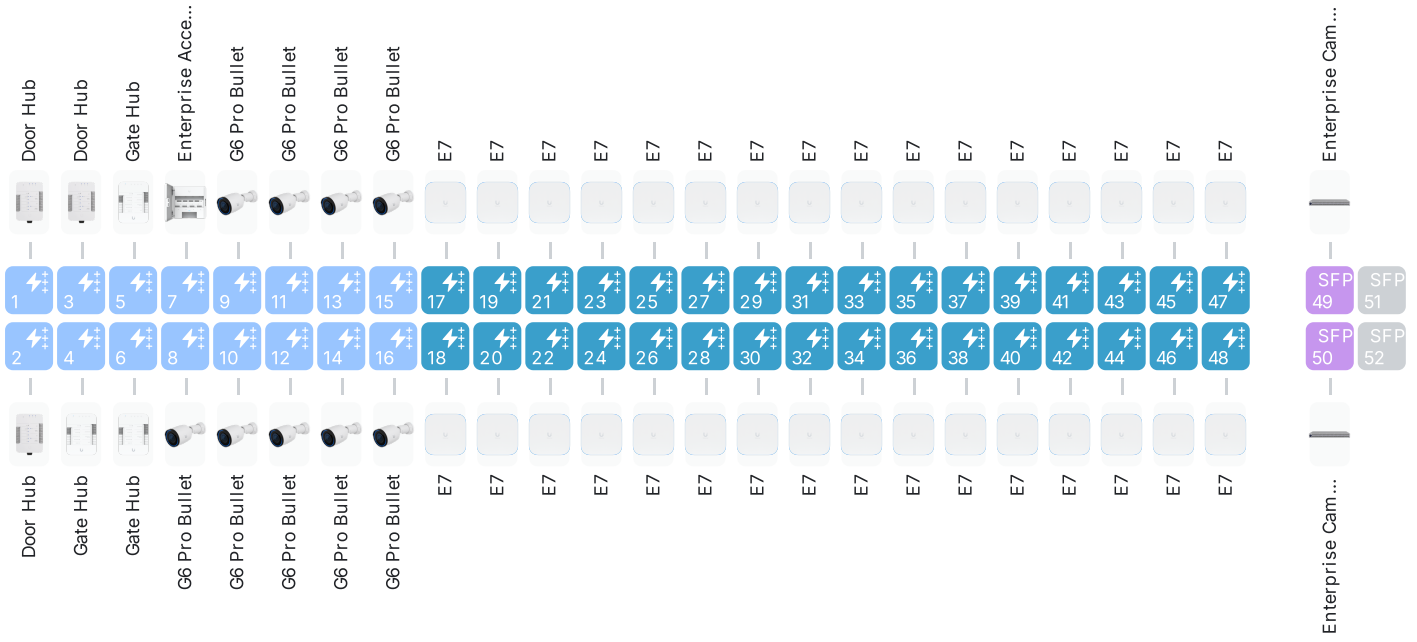

GbE 2.5 GbE 10 GbE 25 GbE 100 GbE PoE PoE+ PoE++ PoE+++ WAN

G Enterprise Campus 48 PoE

PoE Power Used 1596/2150W

H Enterprise Campus 48 PoE

PoE Power Used 793/2150W

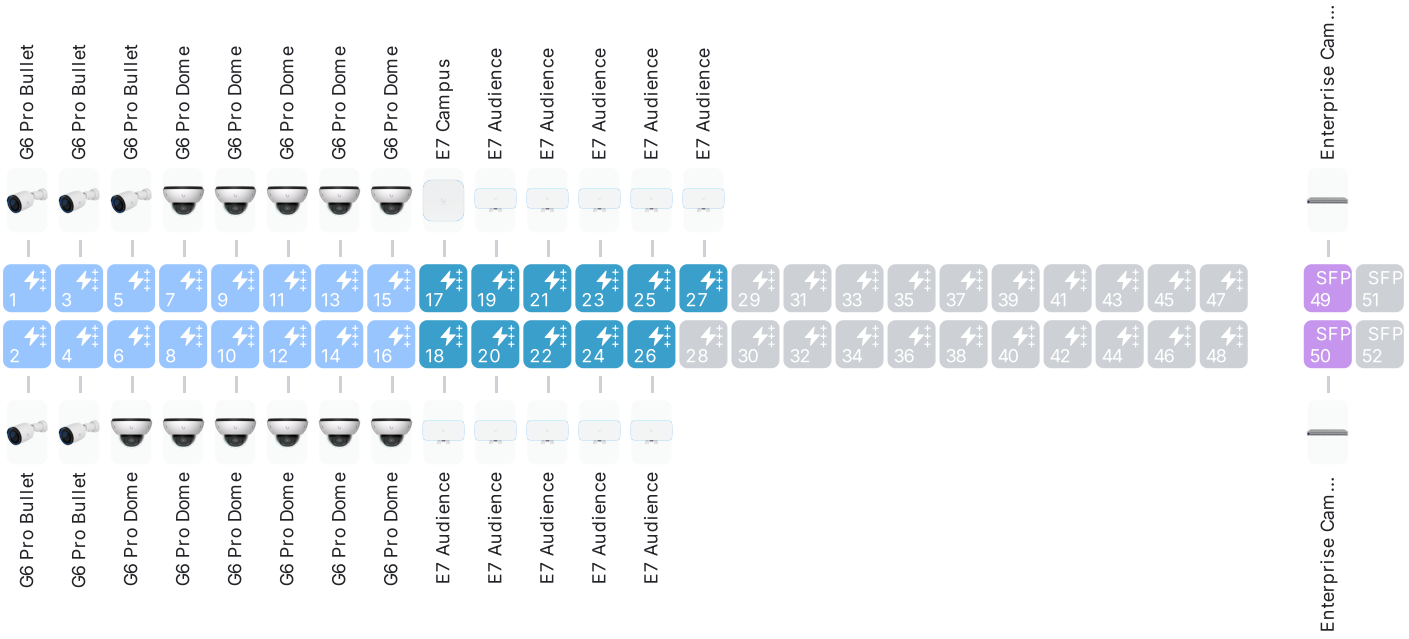

GbE 2.5 GbE 10 GbE 25 GbE 100 GbE PoE PoE+ PoE++ PoE+++ WAN

I Enterprise Campus 48 PoE

PoE Power Used 190/2150W

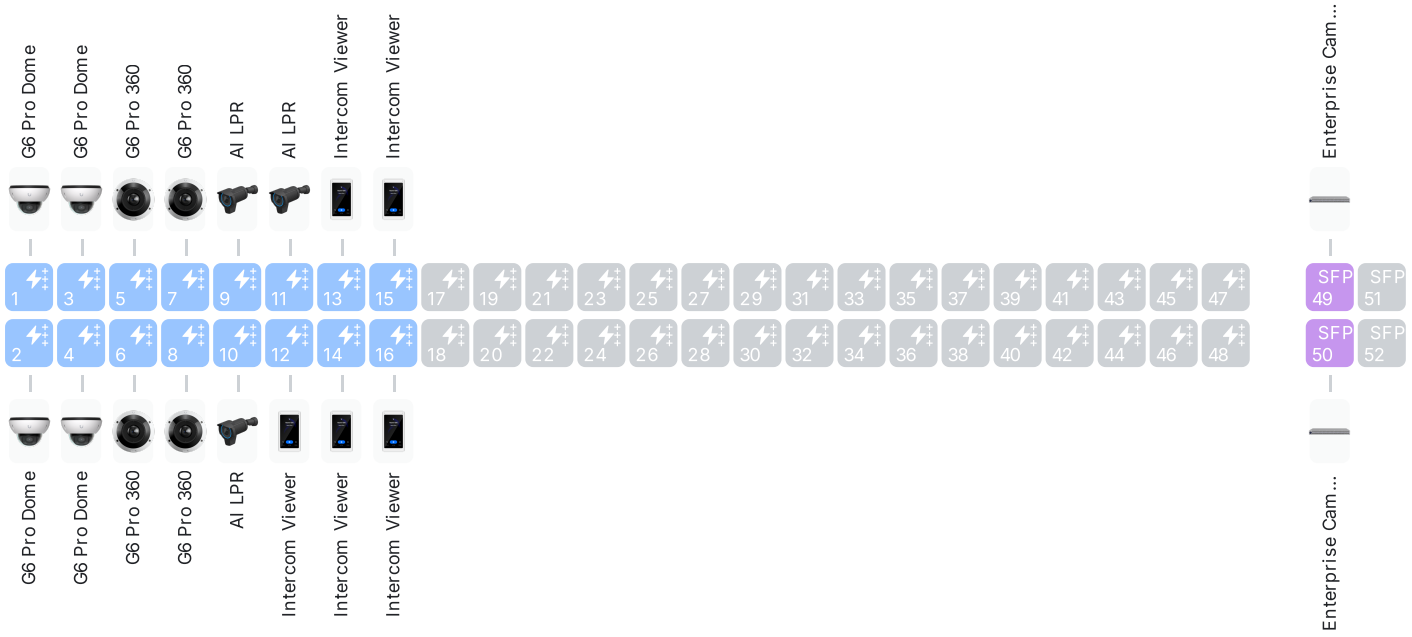

J Enterprise Campus 48 PoE

PoE Power Used 0/2150W

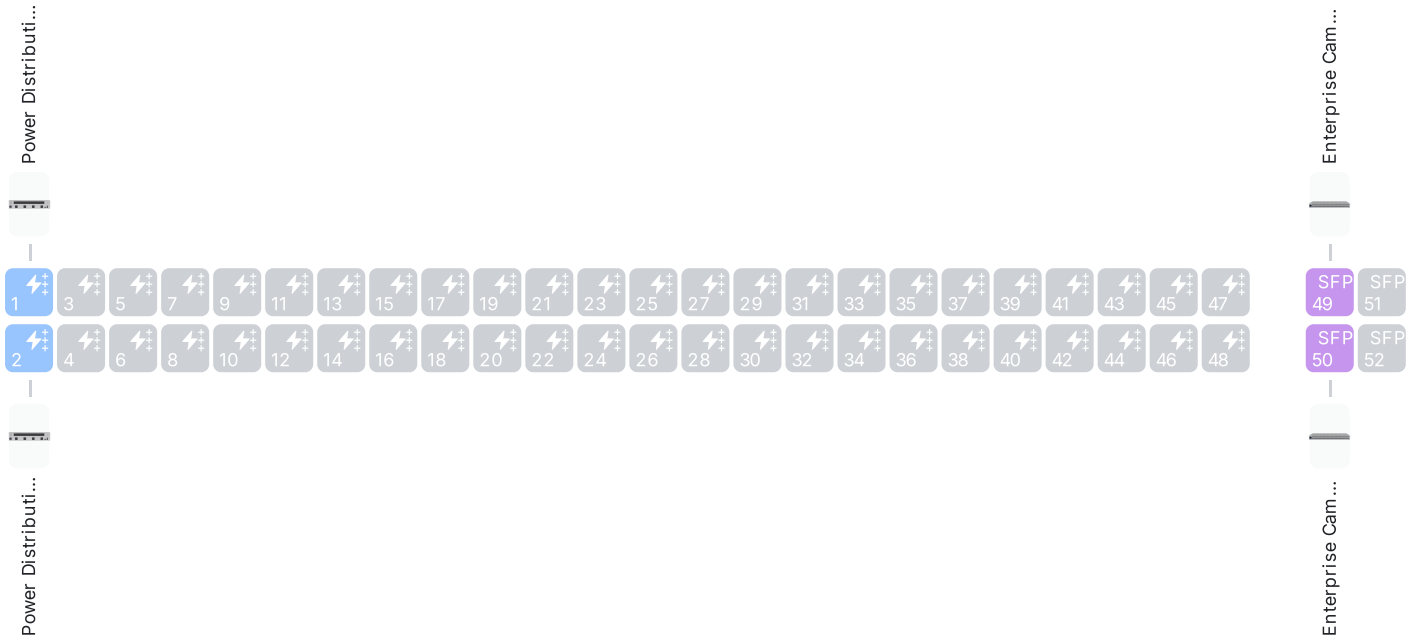

GbE 2.5 GbE 10 GbE 25 GbE 100 GbE PoE PoE+ PoE++ PoE+++ WAN

K Enterprise Campus 48 PoE

PoE Power Used 0/2150W

L Door Hub

PoE Power Used 24/28W

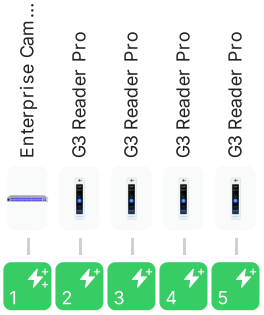

M Door Hub

PoE Power Used 24/28W

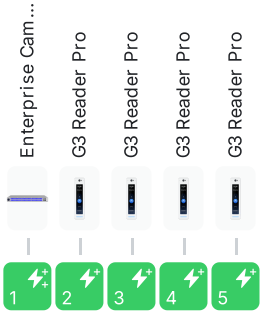

GbE 2.5 GbE 10 GbE 25 GbE 100 GbE PoE PoE+ PoE++ PoE+++ WAN

N Door Hub

PoE Power Used 25/28W

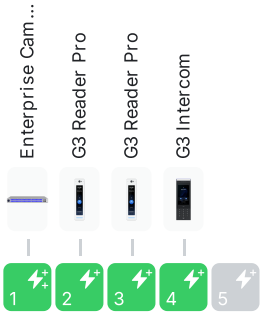

O Enterprise Access Hub

PoE Power Used 0/60W

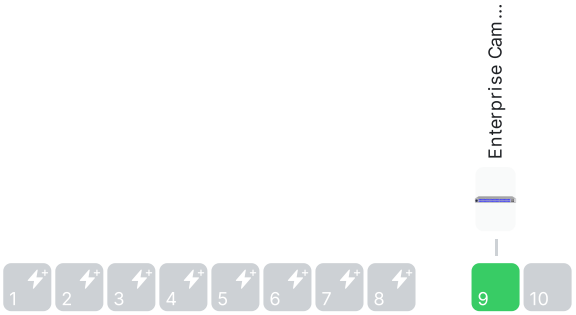

P Gate Hub

PoE Power Used 26/28W

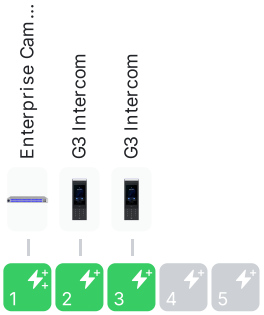

GbE 2.5 GbE 10 GbE 25 GbE 100 GbE PoE PoE+ PoE++ PoE+++ WAN

Q Gate Hub

PoE Power Used 0/28W

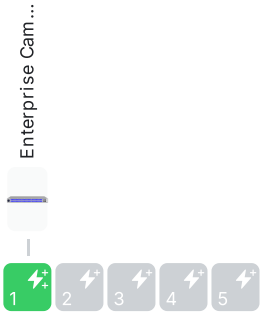

R Gate Hub

PoE Power Used 0/28W

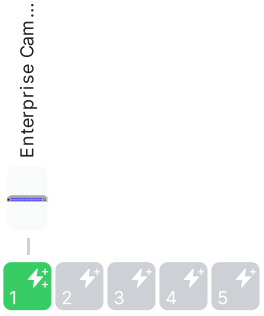

GbE 2.5 GbE 10 GbE 25 GbE 100 GbE PoE PoE+ PoE++ PoE+++ WAN